
Pérgola em cumaru para cotação

ROOFTOP | 4,50 × 3,00 m | 13,50 m² | REVISÃO 04 | 29/10/2026

Alternativa com quatro pilares, dois livres e dois junto ao R02, e travessas mais leves e próximas. Solicitar preços e disponibilidade para as peças abaixo, com dimensões finais após aparelhamento.

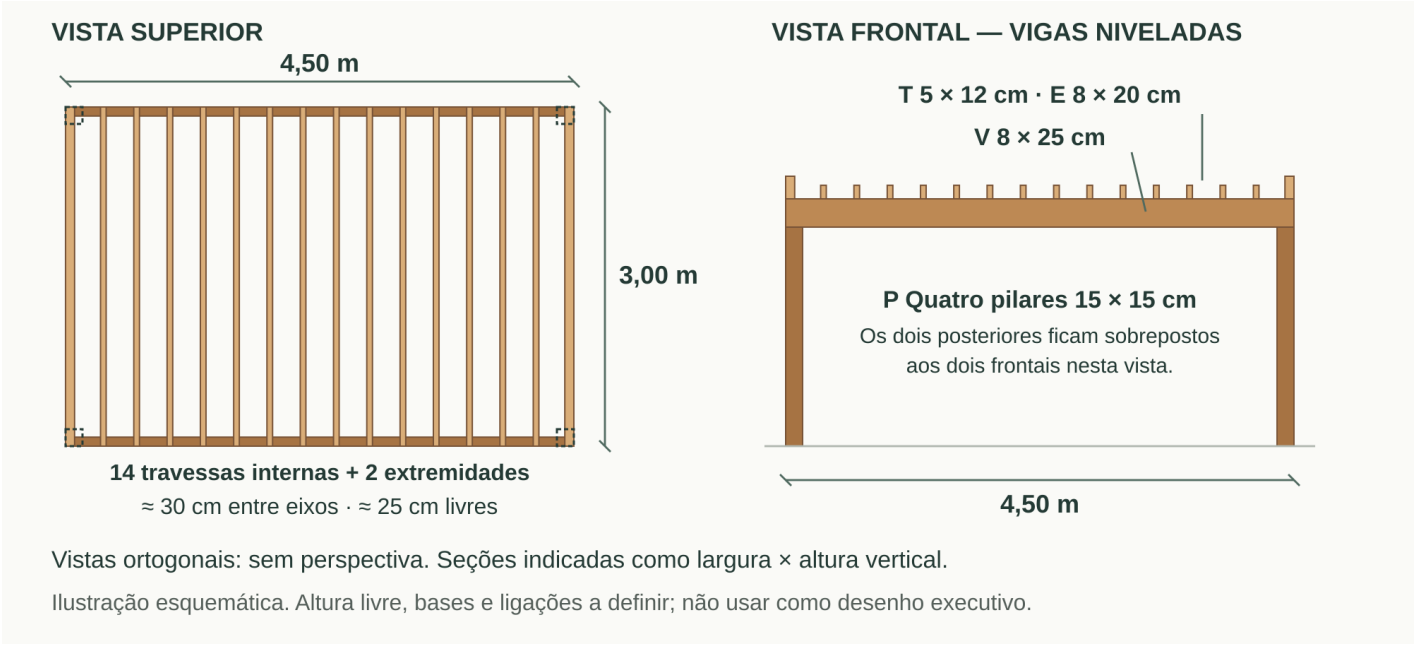

Vistas ortogonais: sem perspectiva. Seções indicadas como largura × altura vertical.

Ilustração esquemática. Altura livre, bases e ligações a definir; não usar como desenho executivo.

Quantitativo preliminar

Ref.	Peça	Qtd.	Seção final	Comprimento unit.
P	Pilares	4	15 × 15 cm	3,00 m*
V	Vigas principais	2	8 × 25 cm	4,50 m
T	Travessas internas	14	5 × 12 cm	3,00 m
E	Travessas de extremidade	2	8 × 20 cm	3,00 m

22 peças | Volume geométrico líquido: 0,798 m³ | Reserva comercial de 10–15%: 0,88–0,92 m³

Nas vigas e travessas, seção = largura × altura vertical. *Pilares de 3,00 m para cotação de estoque; altura livre e comprimentos de corte ainda não definidos.

Espaçamento: 16 linhas transversais no total, sendo 14 internas e 2 extremidades. Aproximadamente 30 cm entre eixos e 25 cm livres entre as internas; ajustar no detalhamento final.

A confirmar na proposta comercial

Disponibilidade, dimensões finais, comprimentos de estoque e condição de secagem da madeira. Discriminar ferragens, bases, contraventamentos, usinagem, acabamento, transporte, içamento e montagem. Não considerar meia-madeira profunda nas vigas principais.

ALTERNATIVA PARA COTAÇÃO — NÃO LIBERA CORTE OU MONTAGEM

Seções sujeitas à validação estrutural, incluindo parreira adulta molhada e frutos, vento, estabilidade, ligações, bases e capacidade da laje. Ilustração sem detalhes executivos de fixação.