
PAVIMENTO GARAGEM | CAD B04

Eixos reconciliados com G02 / R08 | cotas em metros | corte e aberturas preservados

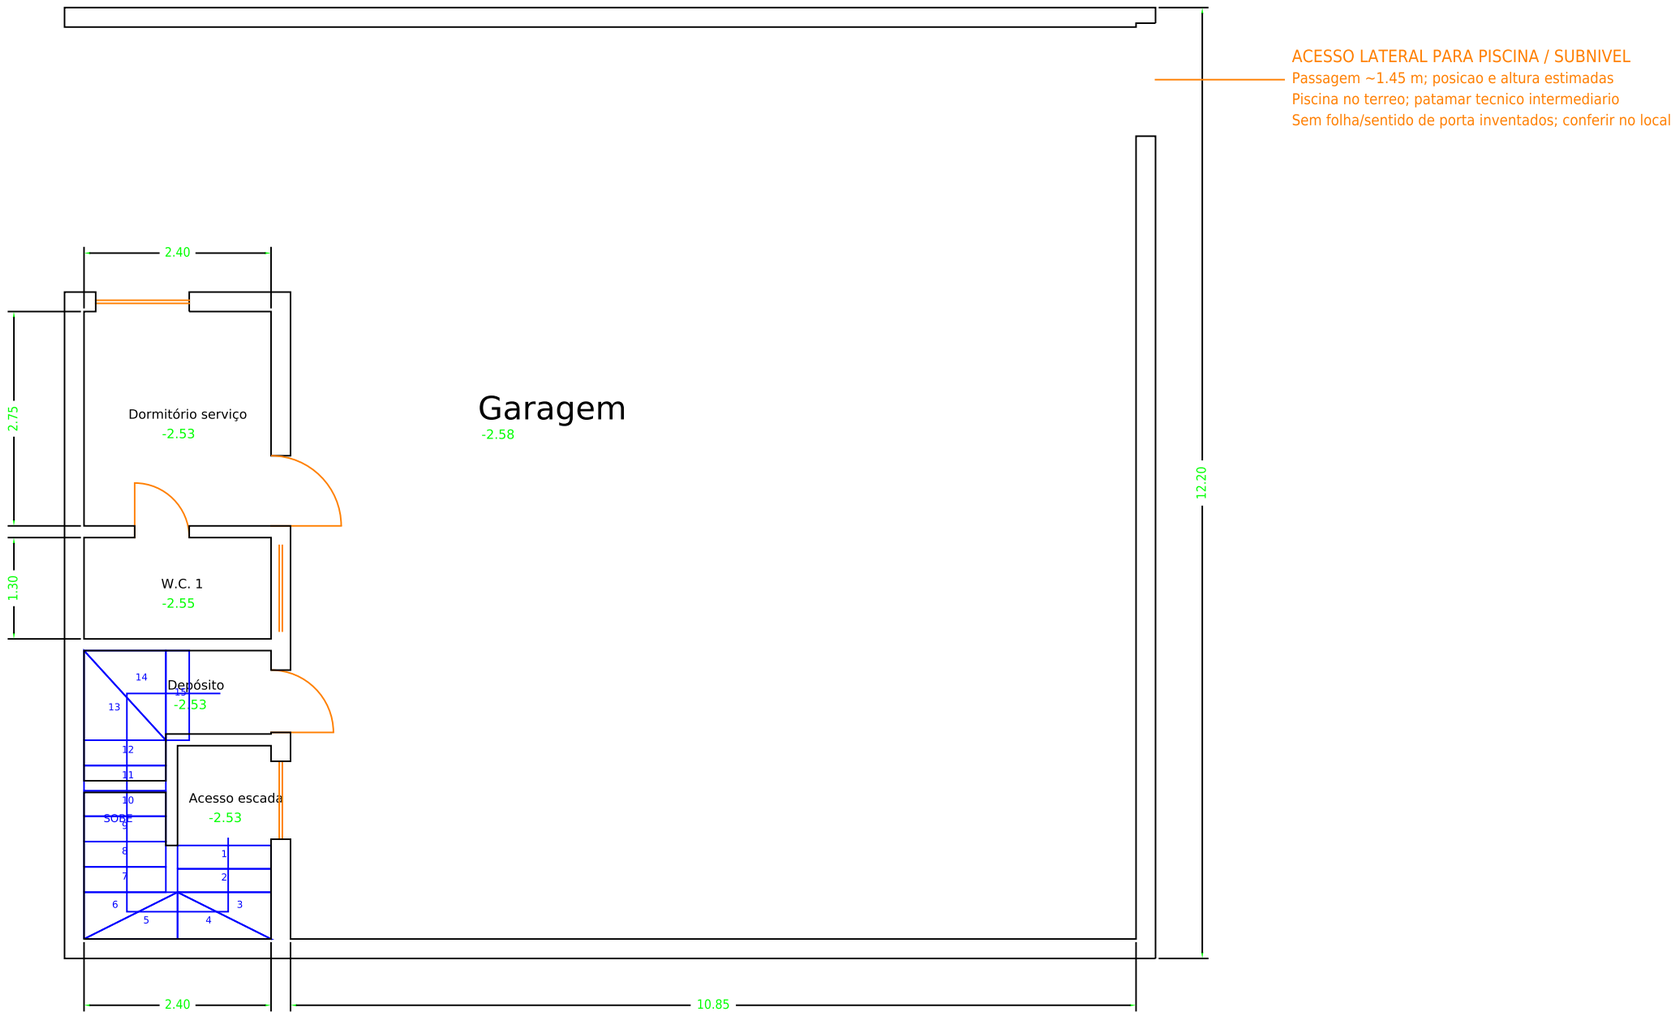

GARAGEM B04 | Reconstrução por cotas e eixos. Não é levantamento executivo.
Base G02/R08 preservada. Mesmo referencial XY. Laje única, sem placas por cômodo.
Garagem: fonte −2.58; norte/rampa −2.63. Quarto/depósito −2.53; WC −2.55.
Escada separada: inicia à direita, contorna ao sul e sobe à esquerda; 13/14 diagonais, 15 reto.
Hipótese: 15 pisos + patamar, 16 espelhos de .18, ligando −2.53 a +.35. Confirmar em campo.
Depósito: principal 2.40 × 1.07; dente 1.05 × .60. Limites marcados pelo usuário preservados.
Teto acompanha o intradorso até o fim da escada, inclusive 13/14/15, conforme confirmação do usuário.
Porta de acesso à escada de CORRER/aberta, sem giro contra degraus, conforme usuário.
Paredes mantidas acima e abaixo das janelas. Espessuras e posições não cotadas são estimadas.
Patamar do novo combinado: borda x0 → .15 para o piso 15. Arquivo G02 não foi alterado.
Garagem 10.85 entre x1.45 e12.30. Parede do bloco .25 inferida; face interna da escada x1.20.
Acesso lateral piscina/sauna representado por fotos: posição e dimensões aproximadas a conferir.
Duto da lareira sem volume, posição pendente. Rampa/arrimos e interpolação de níveis a conferir.