
PAVIMENTO SUPERIOR | CAD R08

Geometria unificada por pavimento | validação por cômodo | PDF exportado do DXF

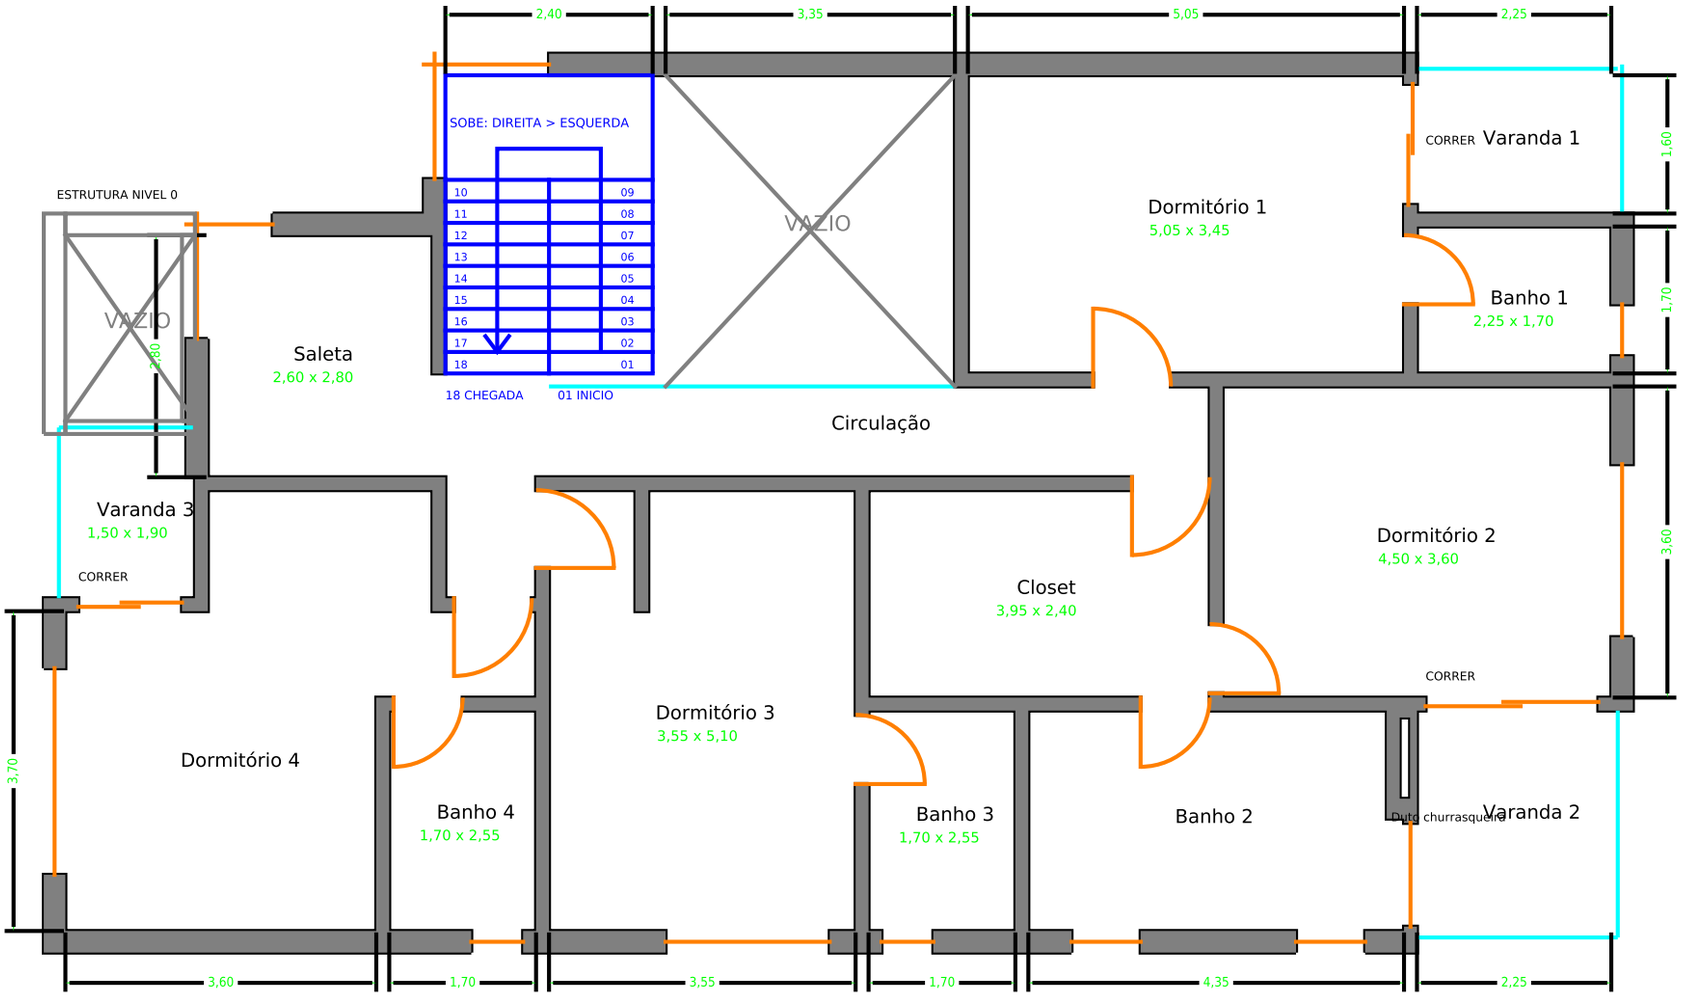

Paredes internas0.15m e externas0.25m inferidas por cotas. Quartos2.70m: cortes A-A/C-C; banhos2.72m: A-A.
Portas sem cota: largura0.80/0.90m, posição e altura estimadas. Janelas cotadas; posições aproximadas.
Banho2 tem ressalto0.20m; posiçãoY=1.30m e duto esquemáticos. Não confundir1.20m do box com ressalto.
Escada AS-BUILT: começa à DIREITA no piso inferior e chega à ESQUERDA no superior, conforme usuário.
Corte B-B: pisos+.35/+3.59, patamar+1.97; desnível3.24m, 18espelhos de.18m. Térreo integrado no modelo combinado.
Circulação AS-BUILT reta, sem curvatura. Guarda-corpo e piso corrigidos; vazios sem piso.
Janela escada: anotação2.90x4.74m; altura relativa−2.64..+2.10m. Não são2.90m confirmados por perna.
Cotas gerais18.40x10.40 fecham com internas0.15m/externas0.25m; espessuras inferidas, sem levantamento.
Escada vazada e corrimãos metálicos confirmados pela foto real; espessura de degraus0.07m apenas visual.
Bordas livres do vazio lateral sem parapeito; vidro norte da Varanda 3 preservado. Contorno estrutural no nível do piso.
AS-BUILT: guarda-corpos de todas as três sacadas em vidro, conforme usuário; ferragens ilustrativas.
R08: todos os três acessos às varandas são portas de correr, conforme usuário. Saleta com L menor no canto noroeste, não janela ocupando toda parede.
Saleta: anotação2.45x1.50,p=.60; pernas internas.75/1.20m estimadas. Janela distinta da alta janela da escada.
Duto lareira: POSICAO PENDENTE. Sem geometria ou marcador; conferir no as-built.
Janela L na escada: configuração sugerida pelo usuário e traço da foto; pernas internas1.20m estimadas, conferir.
Varanda1: leitura1.60m adotada; anotação1.50m também visível, confirmar. Planta documental, não executiva.

R08: laje estrutural única. Face inferior comum+3.44; superfícies+3.59/+3.57/+3.54, sem placas por ambiente.
Borda oeste do vazio alinhada aos4 apoios do Jardim. Vazio livre preservado; geometria de apoio parcialmente inferida.